
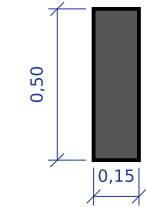


PLANTA BAIXA - NÍVEL ±0,00 (corte a 1,50 m)

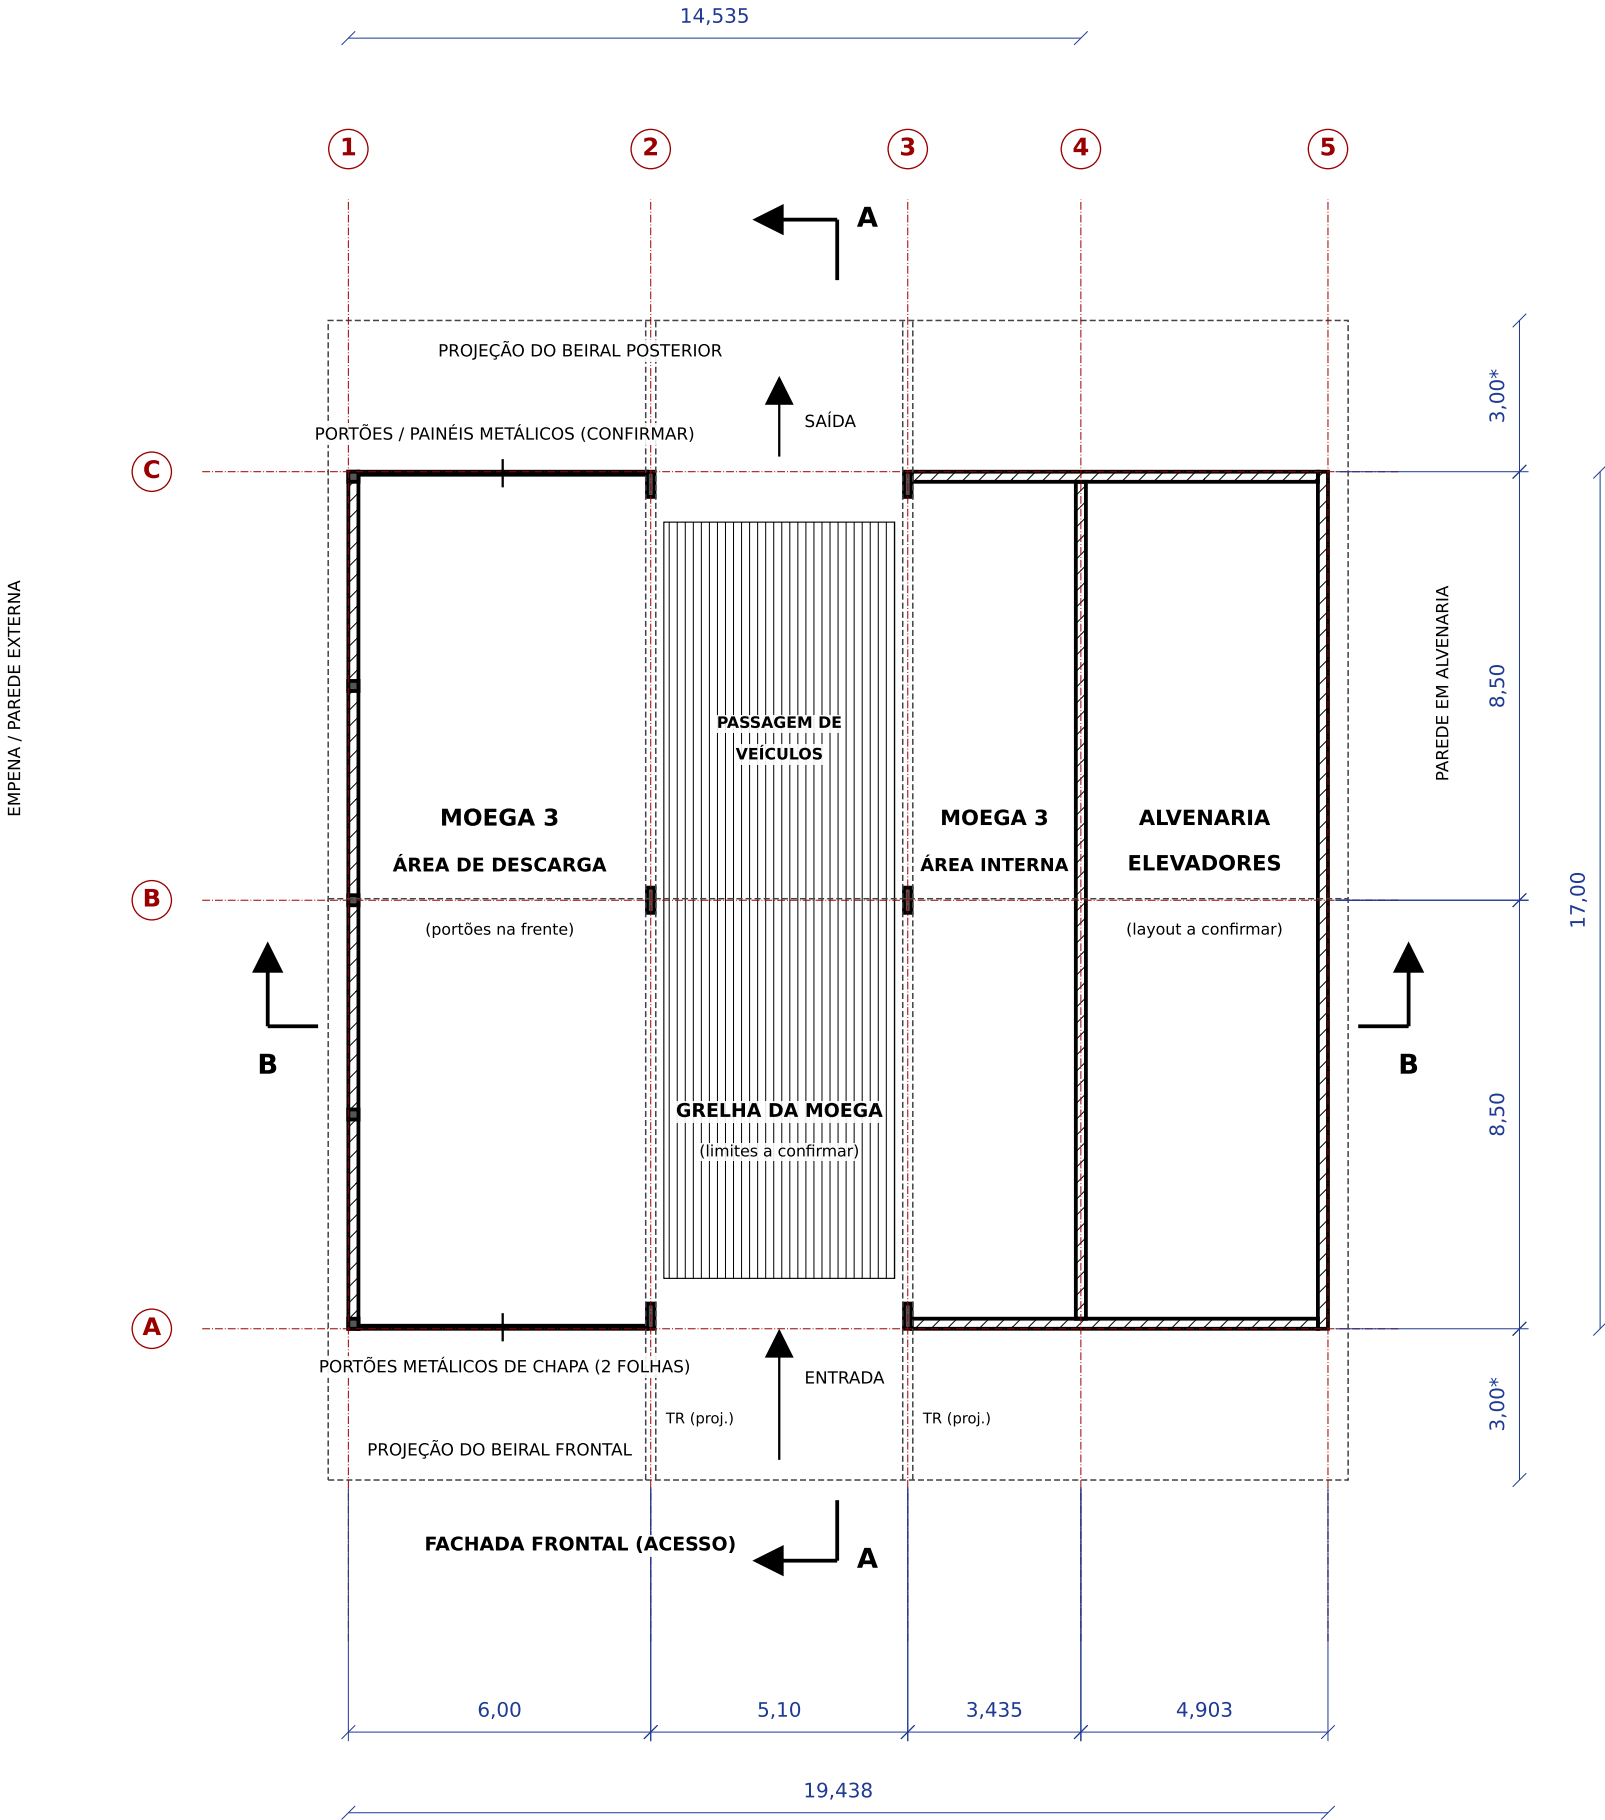

PILAR P (eixos 2 e 3)
seção 150 x 50 - ESC. 1:25
(unidade/material a confirmar)

PLANTA BAIXA

ESC. 1:150

* beirais frontal e posterior 3,00 ("+3" do croqui) - confirmar

NOTAS E PREMISSAS

Levantamento PRELIMINAR elaborado a partir de croqui de campo e registro fotográfico (solo e drone).
Cotas gerais em metros; demais medidas estimadas pelas fotos devem ser conferidas em campo.

Dados do croqui: comprimento 19,438; largura 17,00; vãos a partir da empena externa: 6,000 / 5,100 / 3,435 / 4,903 (parede alvenaria em 14,535); topo dos pilares 4,365; altura total 6,925; pilares 150 x 50 (unidade/material a confirmar).

Valores ADOTADOS (a confirmar):

- beirais frontal e posterior 3,00 em treliça ("+3" do croqui); empenas 0,40;
- alvenaria e = 0,20; treliça h ≈ 0,30 no apoio; Treliças: cantoneira 2" x 3/16" (L 50,8 x 4,76 mm), banzo inferior reto apoiado nos pilares a +4,365.
- portões h ≈ 1,80; inclinação ≈ 25%;
- grelha e fosso da moega: limites indicativos.

LEGENDA

- Alvenaria / concreto (cortado)
- Pilar 150 x 50
- Grelha da moega (indicativa)
- Projeção / elemento oculto
- Eixo estrutural

Unidades: metros (m) • Responsável técnico: _____

CLIENTE
TREVISAN - ARROZ

OBRA / LOCAL
MOEGA 3 - RECEBIMENTO DE GRÃOS

CONTEÚDO
PLANTA BAIXA


SITUAÇÃO
LEVANTAMENTO PRELIMINAR - PARA CONFERÊNCIA

ESCALA
1:150

DATA
25/09/2026

FOLHA
01/08

VISTA SUPERIOR - PLANTA DE COBERTURA

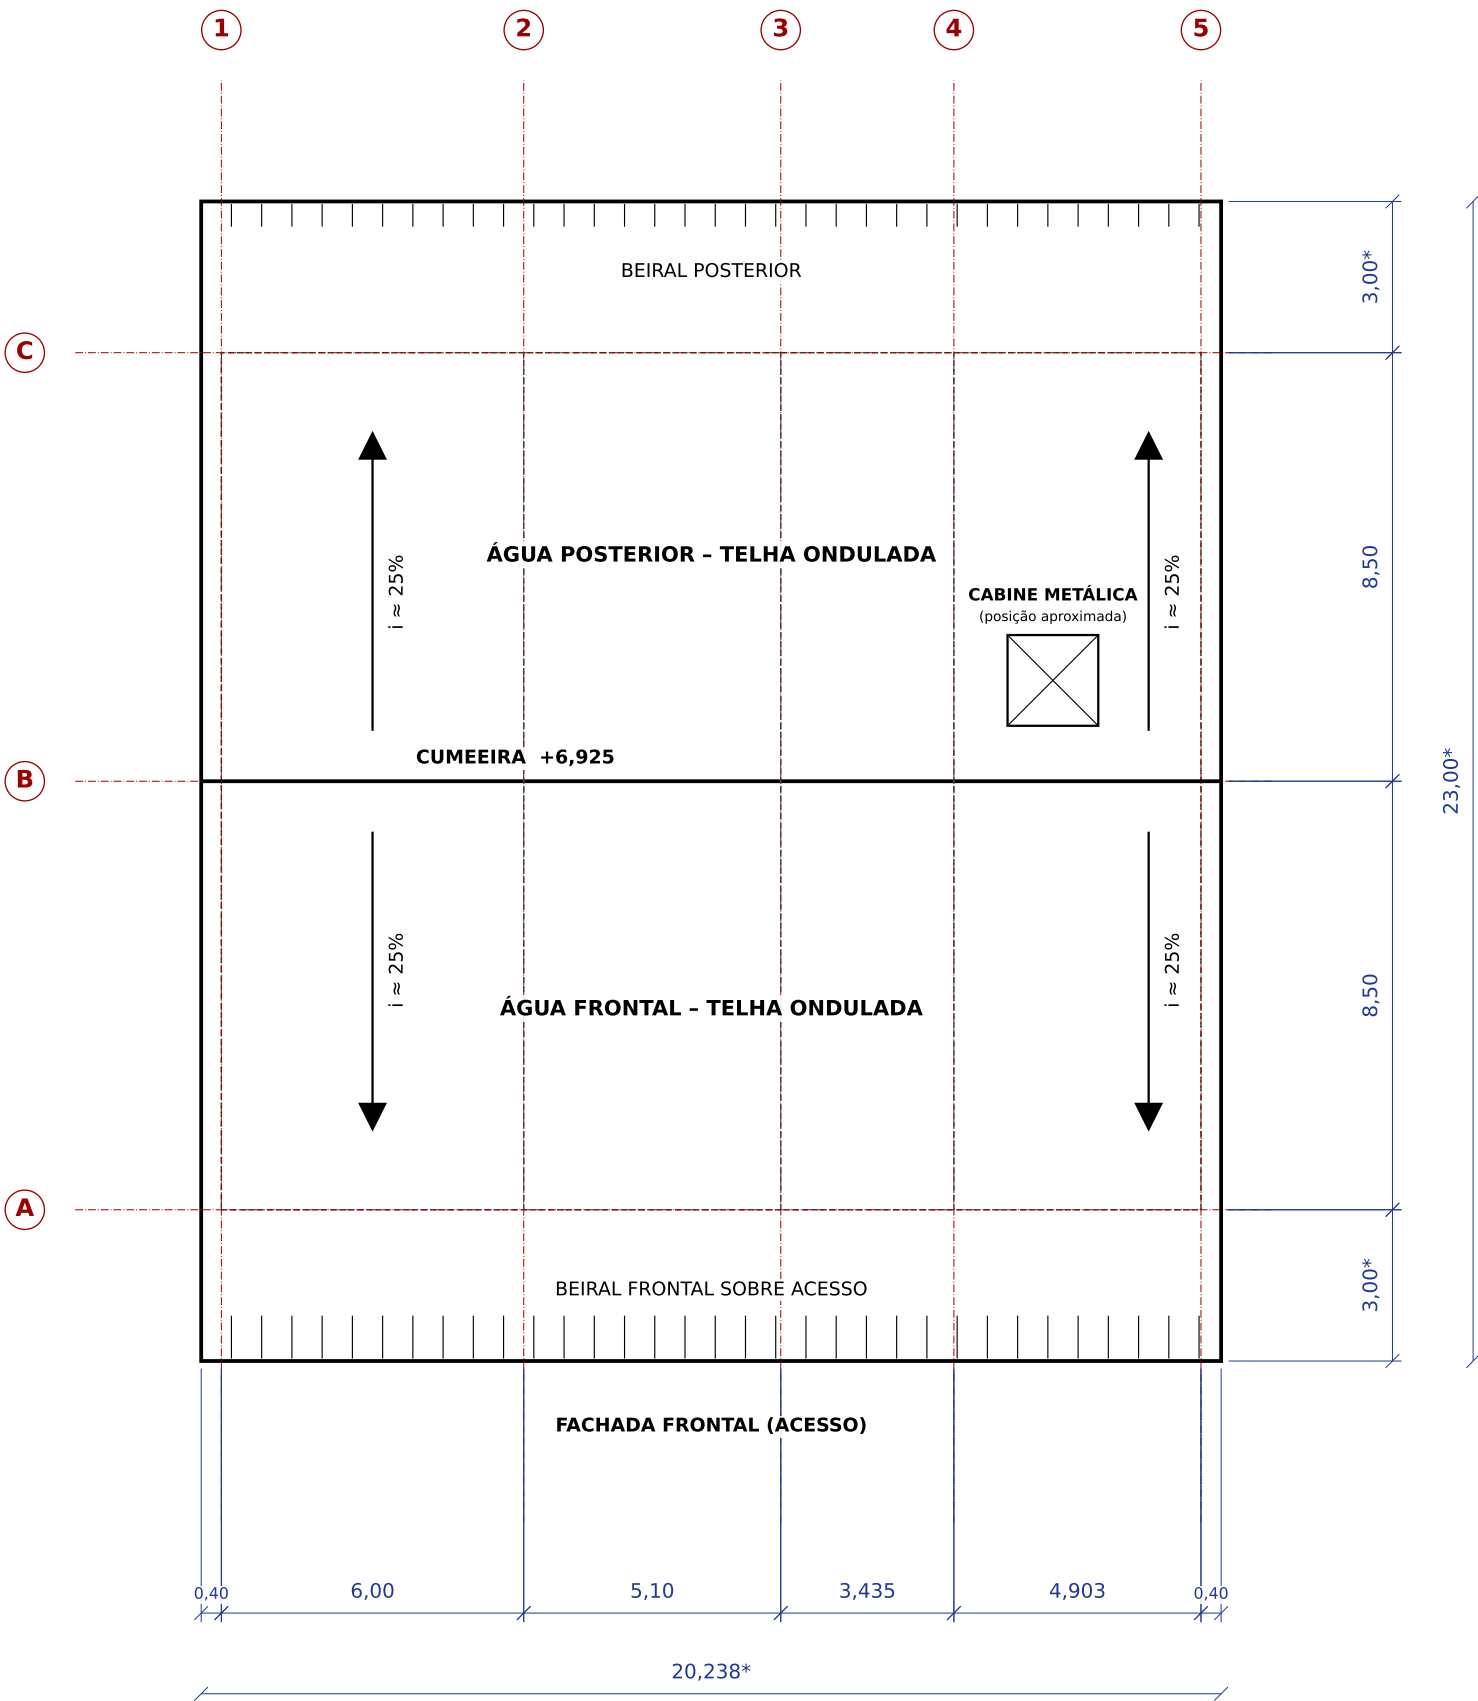

VISTA SUPERIOR / COBERTURA

ESC. 1:150

* dimensões de beiral adotadas - confirmar em campo

NOTAS E PREMISSAS

Levantamento PRELIMINAR elaborado a partir de croqui de campo e registro fotográfico (solo e drone).
Cotas gerais em metros; demais medidas estimadas pelas fotos devem ser conferidas em campo.

Dados do croqui: comprimento 19,438; largura 17,00; vãos a partir da empena externa: 6,000 / 5,100 / 3,435 / 4,903 (parede alvenaria em 14,535); topo dos pilares 4,365; altura total 6,925; pilares 150 × 50 (unidade/material a confirmar).

Valores ADOTADOS (a confirmar):

- beirais frontal e posterior 3,00 em treliça (" +3" do croqui); empenas 0,40;
- alvenaria e = 0,20; treliça h ≈ 0,30 no apoio; Treliças: cantoneira 2" × 3/16" (L 50,8 × 4,76 mm), banzo inferior reto apoiado nos pilares a +4,365.
- portões h ≈ 1,80; inclinação ≈ 25%;
- grelha e fosso da moega: limites indicativos.

LEGENDA

- Alvenaria / concreto (cortado)
- Pilar 150 × 50
- Grelha da moega (indicativa)
- Projeção / elemento oculto
- Eixo estrutural

Unidades: metros (m) • Responsável técnico: _____

CLIENTE
TREVISAN - ARROZ

OBRA / LOCAL
MOEGA 3 - RECEBIMENTO DE GRÃOS

CONTEÚDO
VISTA SUPERIOR - COBERTURA


SITUAÇÃO
LEVANTAMENTO PRELIMINAR - PARA CONFERÊNCIA

ESCALA
1:150

DATA
25/09/2026


FOLHA
02/08

VISTAS - FRONTAL E LATERAL ESQUERDA

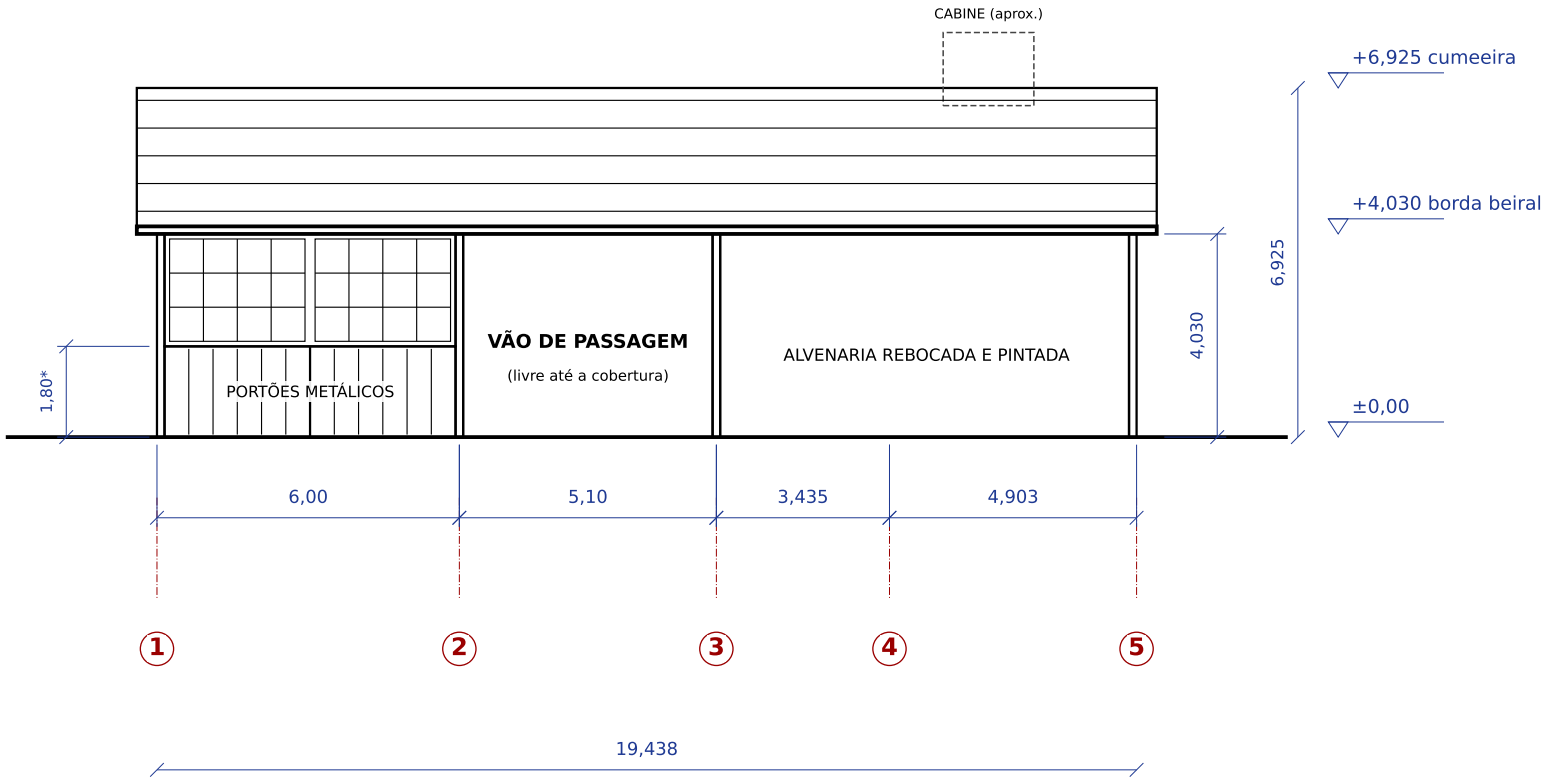

VISTA FRONTAL

ESC. 1:150

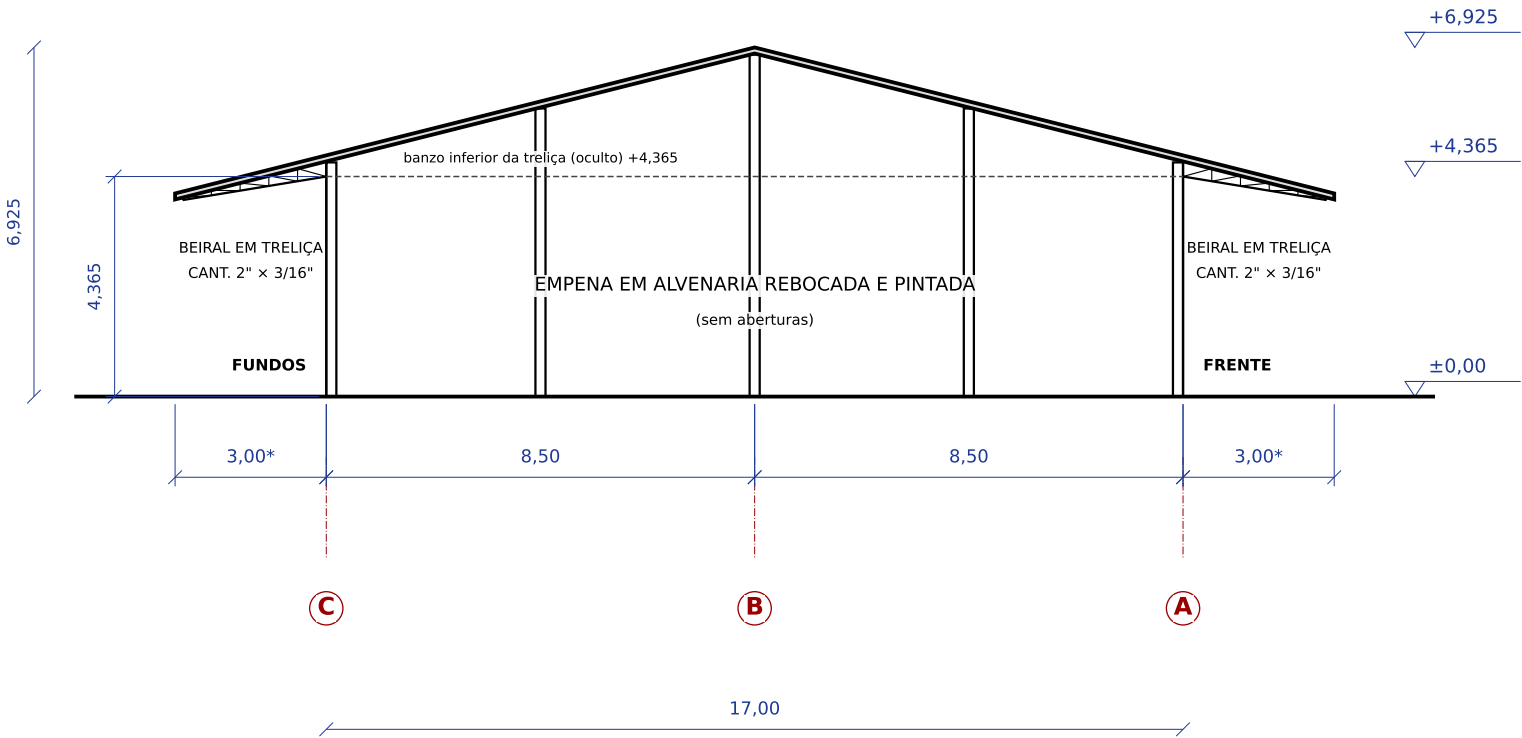

VISTA LATERAL ESQUERDA (EIXO 1)

ESC. 1:150

NOTAS E PREMISSAS

Levantamento PRELIMINAR elaborado a partir de croqui de campo e registro fotográfico (solo e drone). Cotas gerais em metros; demais medidas estimadas pelas fotos devem ser conferidas em campo.

Dados do croqui: comprimento 19,438; largura 17,00; vãos a partir da empena externa: 6,000 / 5,100 / 3,435 / 4,903 (parede alvenaria em 14,535); topo dos pilares 4,365; altura total 6,925; pilares 150 x 50 (unidade/material a confirmar).

Valores ADOTADOS (a confirmar):

- beirais frontal e posterior 3,00 em treliça (" +3" do croqui); empenas 0,40;
- alvenaria e = 0,20; treliça h ≈ 0,30 no apoio; Treliças: cantoneira 2" x 3/16" (L 50,8 x 4,76 mm), banzo inferior reto apoiado nos pilares a +4,365.
- portões h ≈ 1,80; inclinação ≈ 25%;
- grelha e fosso da moega: limites indicativos.

LEGENDA

- Alvenaria / concreto (cortado)
- Pilar 150 x 50
- Grelha da moega (indicativa)
- Projeção / elemento oculto
- Eixo estrutural

Unidades: metros (m) • Responsável técnico: _____

CLIENTE
TREVISAN - ARROZ

OBRA / LOCAL
MOEGA 3 - RECEBIMENTO DE GRÃOS

CONTEÚDO
VISTAS FRONTAL E LATERAL


SITUAÇÃO
LEVANTAMENTO PRELIMINAR - PARA CONFERÊNCIA

ESCALA
1:150

DATA
25/09/2026


FOLHA
03/08

CORTES - TRANSVERSAL (AA) E LONGITUDINAL (BB)

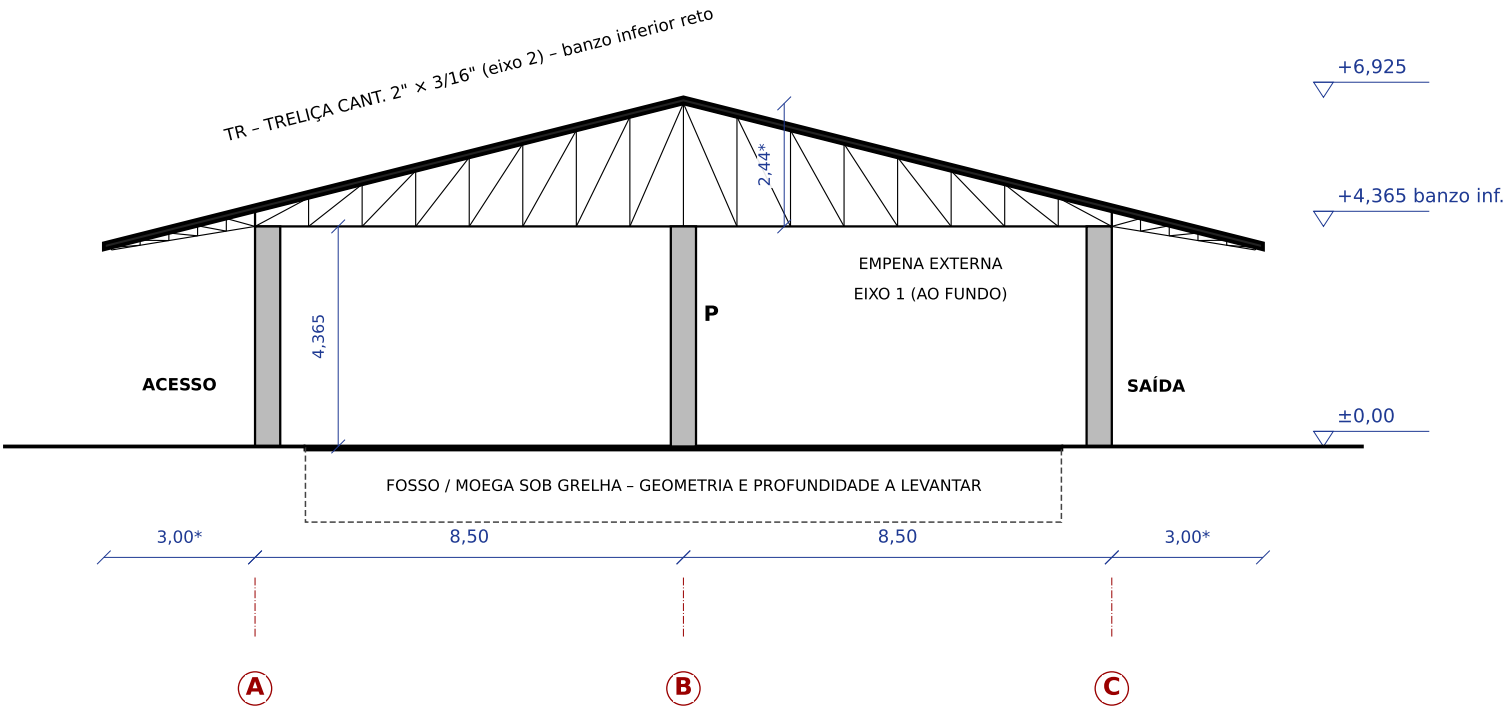

CORTE AA (TRANSVERSAL)

ESC. 1:150

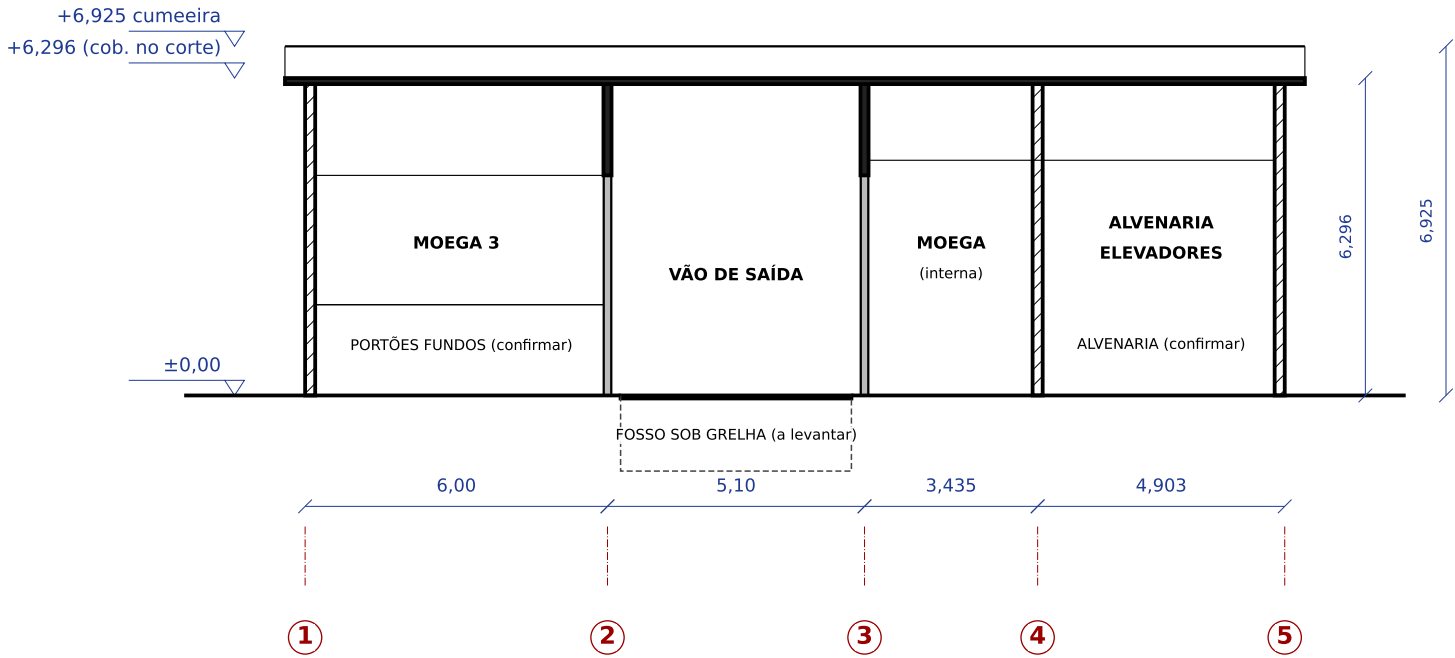

CORTE BB (LONGITUDINAL)

ESC. 1:150

NOTAS E PREMISSAS

Levantamento PRELIMINAR elaborado a partir de croqui de campo e registro fotográfico (solo e drone).
Cotas gerais em metros; demais medidas estimadas pelas fotos devem ser conferidas em campo.

Dados do croqui: comprimento 19,438; largura 17,00; vãos a partir da empena externa: 6,000 / 5,100 / 3,435 / 4,903 (parede alvenaria em 14,535); topo dos pilares 4,365; altura total 6,925; pilares 150 x 50 (unidade/material a confirmar).

Valores ADOTADOS (a confirmar):

- beirais frontal e posterior 3,00 em treliça (" +3" do croqui); empenas 0,40;
- alvenaria e = 0,20; treliça h ≈ 0,30 no apoio;
- Treliças: cantoneira 2" x 3/16" (L 50,8 x 4,76 mm), banzo inferior reto apoiado nos pilares a +4,365.
- portões h ≈ 1,80; inclinação ≈ 25%;
- grelha e fosso da moega: limites indicativos.

LEGENDA

- Alvenaria / concreto (cortado)
- Pilar 150 x 50
- Grelha da moega (indicativa)
- Projeção / elemento oculto
- Eixo estrutural

Unidades: metros (m) • Responsável técnico: _____

CLIENTE
TREVISAN - ARROZ


OBRA / LOCAL
MOEGA 3 - RECEBIMENTO DE GRÃOS

CONTEÚDO
CORTES AA E BB

SITUAÇÃO
LEVANTAMENTO PRELIMINAR - PARA CONFERÊNCIA


ESCALA 1:150	DATA 25/09/2026	FOLHA 04/08
------------------------	---------------------------	-----------------------

PLANTA DE COBERTURA GERAL - COMPLEXO TREVISAN (GEORREFERENCIADA)

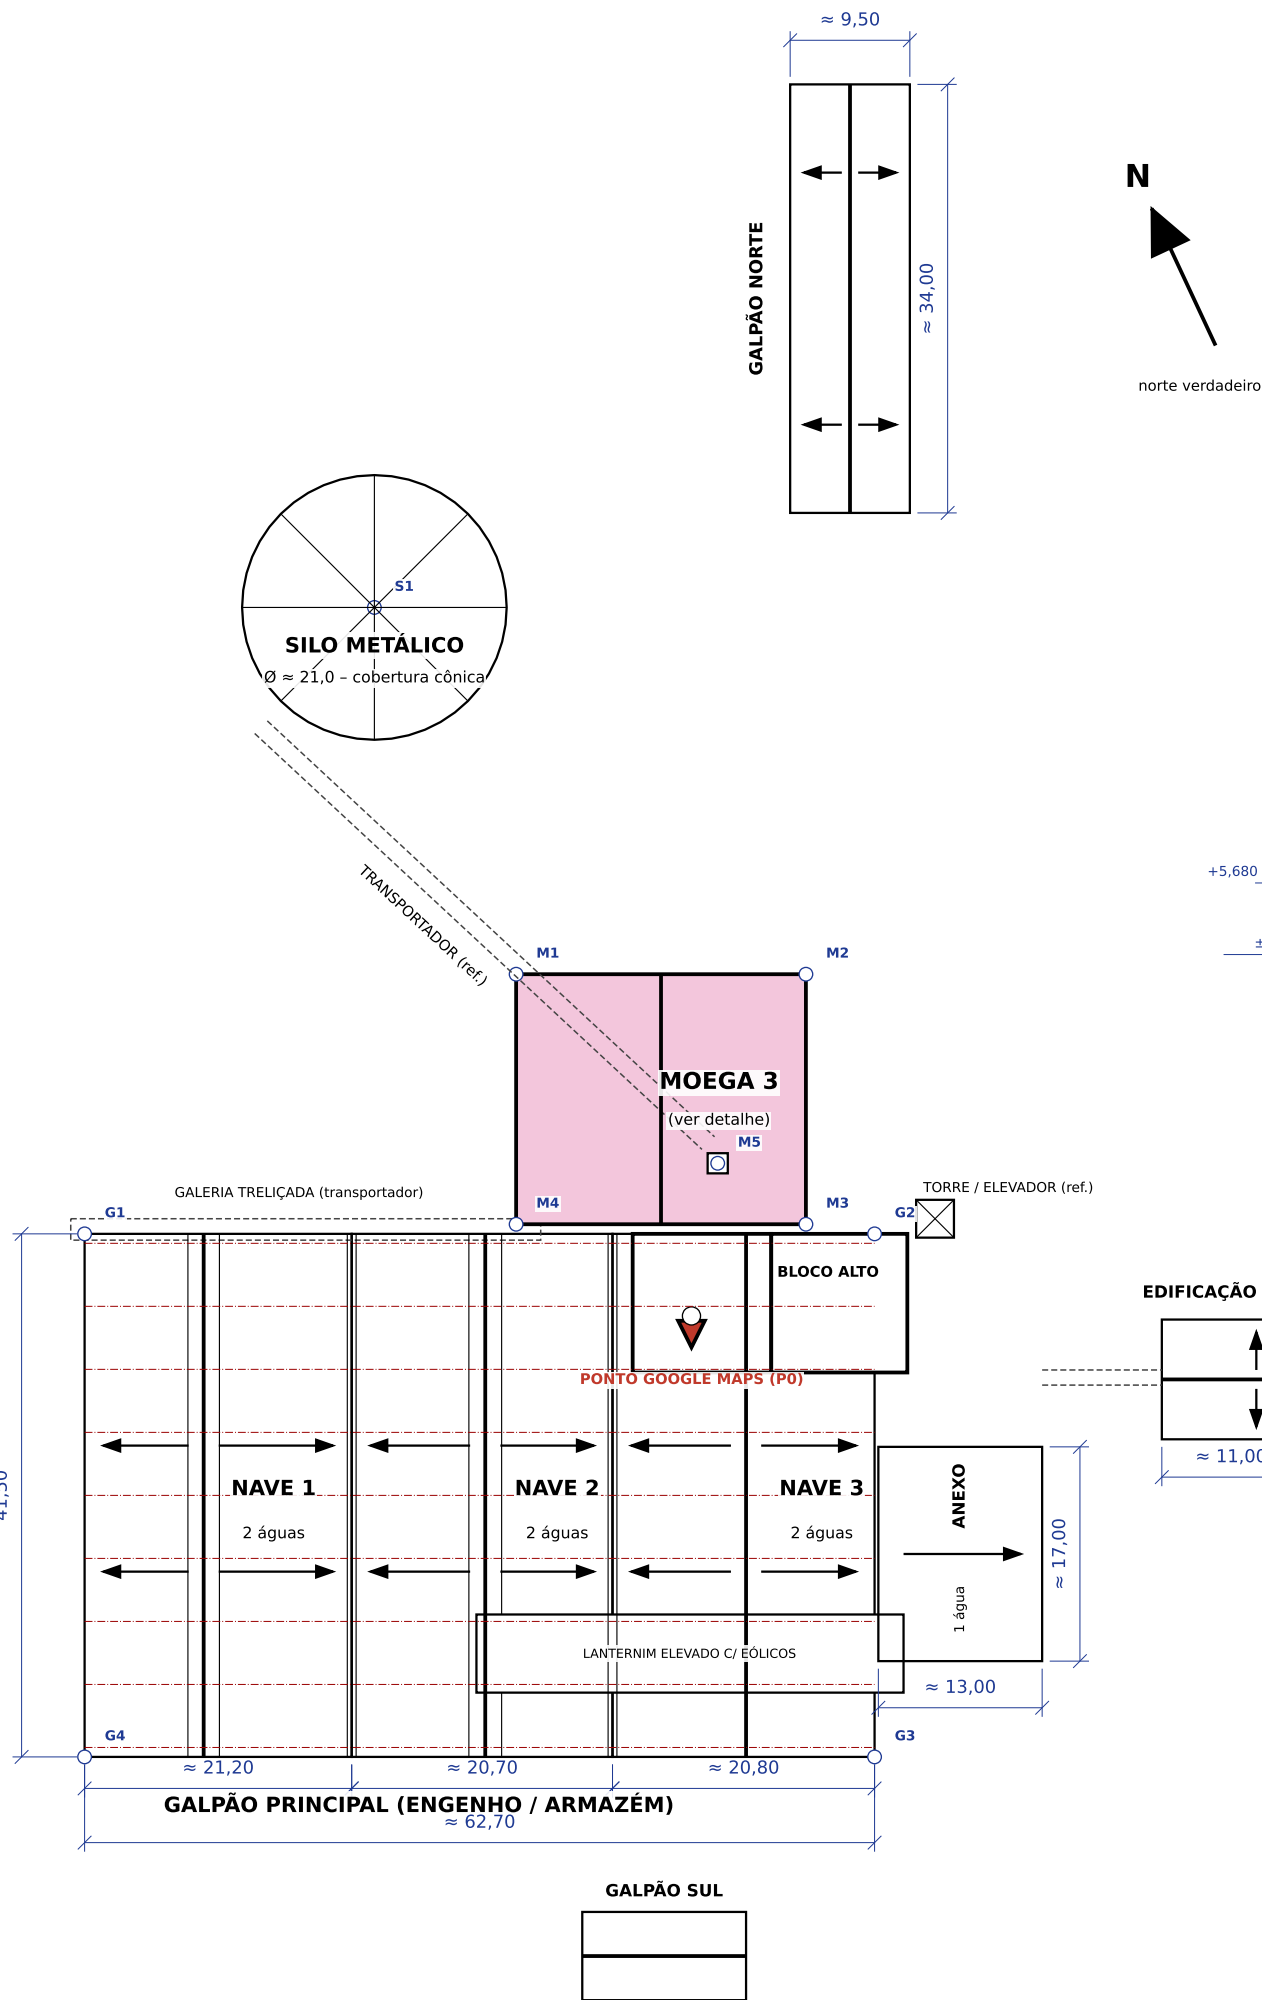

COORDENADAS DOS VÉRTICES (WGS-84)

PONTO	DESCRIÇÃO	LATITUDE	LONGITUDE
P0	Ponto Google Maps	-30.048300	-52.919350
M1	Moega - canto NO (beiral)	-30.048006	-52.919351
M2	Moega - canto NE (beiral)	-30.048093	-52.919134
M3	Moega - canto SE (beiral)	-30.048255	-52.919221
M4	Moega - canto SO (beiral)	-30.048167	-52.919438
M5	Moega - torre treliçada	-30.048189	-52.919266
G1	Galpão princ. - canto NO	-30.048043	-52.919763
G2	Galpão princ. - canto NE	-30.048282	-52.919173
G3	Galpão princ. - canto SE	-30.048619	-52.919355
G4	Galpão princ. - canto SO	-30.048381	-52.919945
S1	Silo - centro (Ø ≈ 21,0)	-30.047726	-52.919329

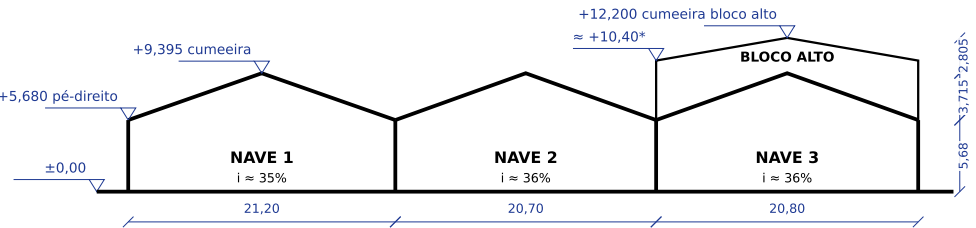

CORTE ESQUEMÁTICO - GALPÃO PRINCIPAL

ESC. 1:600

QUADRO DE ALTURAS (m) - rascunho de campo

ELEMENTO	PÉ-DIREITO	CUMEEIRA	INCLINAÇÃO	ORIGEM
Nave 1	+5,680	+9,395	≈ 35%	rascunho
Nave 2	+5,680	+9,395	≈ 36%	rascunho
Nave 3	+5,680	+9,395	≈ 36%	rascunho
Bloco alto	≈ +10,40*	+12,200	-	rascunho
Lant. elevado	+9,395 (beiral)	≈ +10,20*	≈ 26%	drone
Moega 3	+4,365	+6,925	≈ 25%	croqui

* valores estimados (rascunho / drone) - medir em campo

COBERTURA GERAL

ESC. 1:600

NOTAS E PREMISSAS

Planta GEORREFERENCIADA pelo ponto do Google Maps (Indústria Trevisan Alimentos):
-30.0482997 / -52.9193496
(30°02'53.88"S 52°55'09.66"O).
O ponto cai sobre a NAVE 3 do galpão principal.

Base: satélite retificado + drone zenital.
Edificações vizinhas: precisão ± 0,50 a 1,00 m.
Somente a MOEGA 3 possui medidas de campo.

Caimentos, cumeeiras e calhas interpretados pela imagem e pelas fotos de drone (a confirmar).
Frente da moega (portões) a oeste (drone).

Treliças do galpão a cada 5,00 c/c (traço-ponto).
Alturas das naves e do bloco alto: rascunho de campo (pé-direito 5,680; cumeeira 9,395; bloco alto 12,200). Detalhes: folha 06; estrutura: folha 07.

LEGENDA

- Cobertura da Moega 3 (medida em campo)
- Contorno de cobertura (imagem)
- Cumeeira
- Calha / água-furtada
- Sentido de caimento (a confirmar)
- Transportador / projeção

Unidades: metros (m) • Responsável técnico: _____

CLIENTE
TREVISAN - ARROZ

OBRA / LOCAL
COMPLEXO INDUSTRIAL - MOEGA 3

CONTEÚDO
PLANTA DE COBERTURA GERAL


SITUAÇÃO
LEVANTAMENTO PRELIMINAR - PARA CONFERÊNCIA

ESCALA
1:600

DATA
25/09/2026


FOLHA
05/08

DETALHES DE COBERTURA - COM MEDIDAS

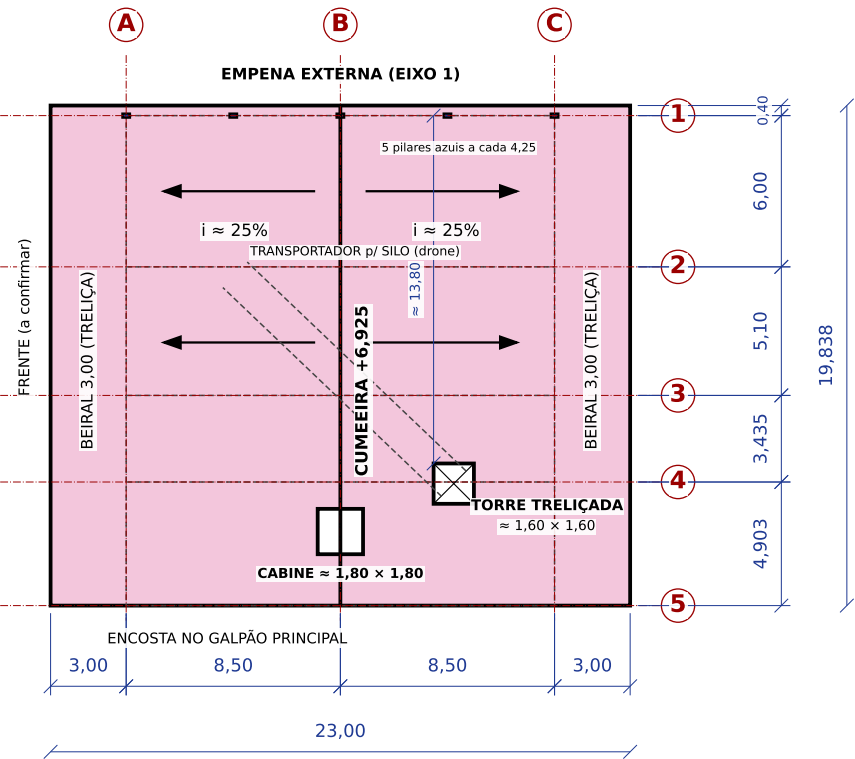

D1 - MOEGA 3 (campo + drone)

ESC. 1:300

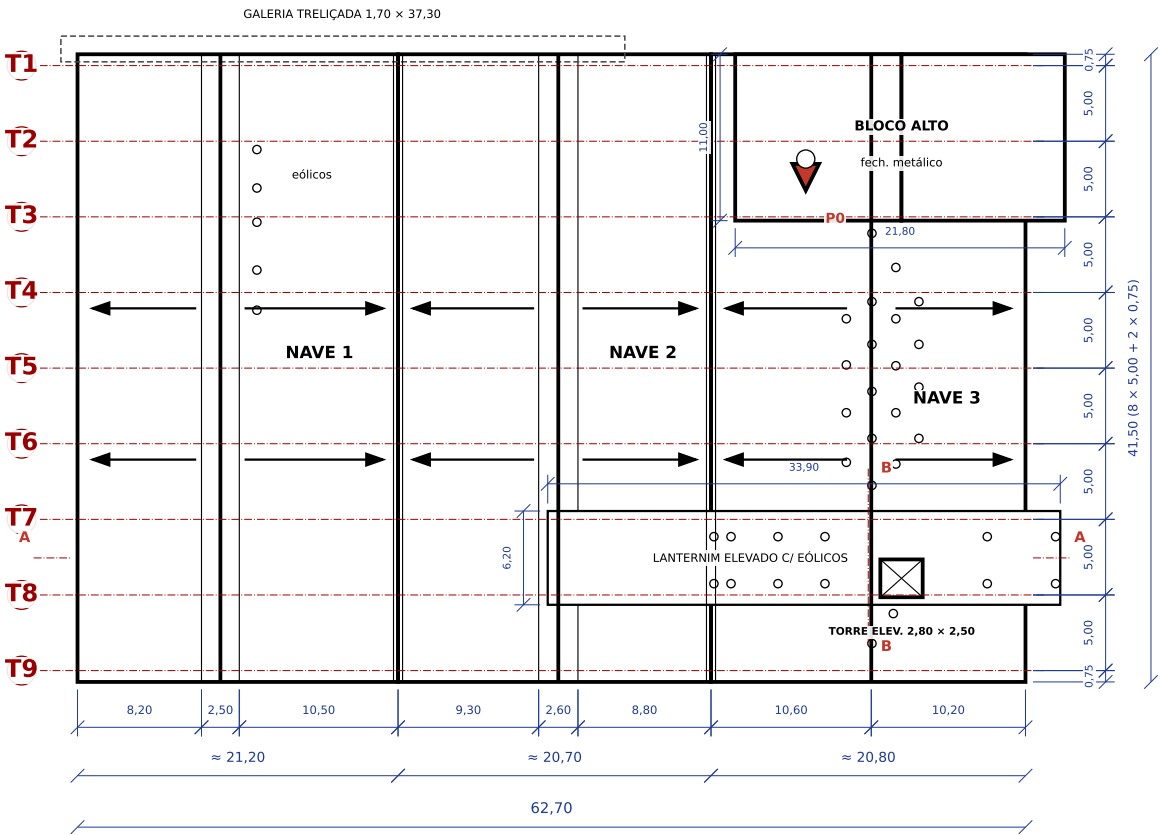


D2 - GALPÃO PRINCIPAL (drone zenital)

ESC. 1:500

QUADRO DE ALTURAS (m) - rascunho de campo


ELEMENTO	PÉ-DIREITO	CUMEEIRA	INCLINAÇÃO	ORIGEM
Nave 1	+5,680	+9,395	≈ 35%	rascunho
Nave 2	+5,680	+9,395	≈ 36%	rascunho
Nave 3	+5,680	+9,395	≈ 36%	rascunho
Bloco alto	≈ +10,40*	+12,200	-	rascunho
Lant. elevado	+9,395 (beiral)	≈ +10,20*	≈ 26%	drone
Moega 3	+4,365	+6,925	≈ 25%	croqui

* valores estimados (rascunho / drone) - medir em campo

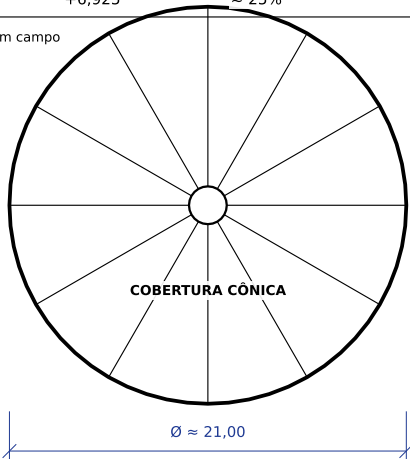


D7 - SILO METÁLICO

ESC. 1:400

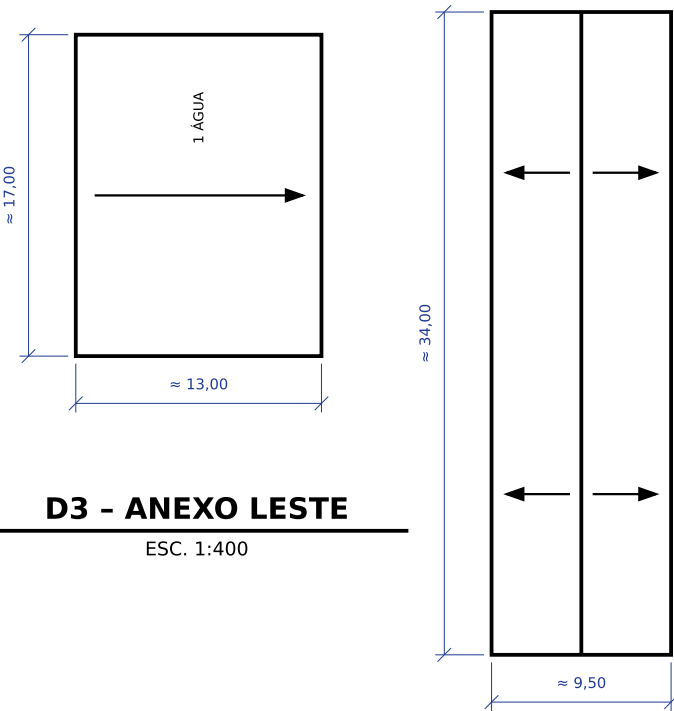


D3 - ANEXO LESTE

ESC. 1:400

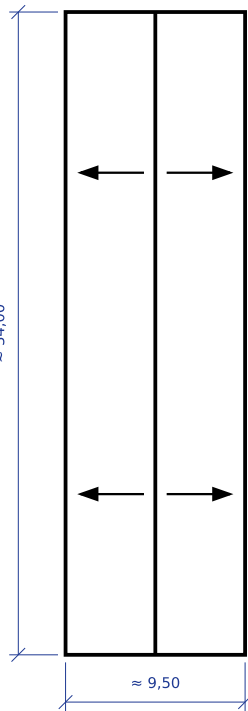


D4 - GALPÃO NORTE

ESC. 1:400

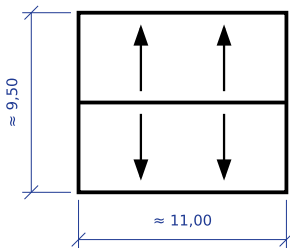

D5 - EDIFICAÇÃO LESTE

ESC. 1:400

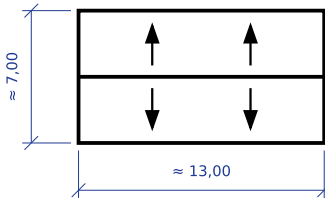

D6 - GALPÃO SUL

ESC. 1:400

NOTAS E PREMISSAS

Detalhes de cobertura com medidas.

Moega 3: medidas de campo (croqui) + pontos novos identificados nas fotos de drone (torre treliçada, cabine, transportador, pilares azuis da empina) - dimensões desses pontos estimadas pela proporção da foto.

Demais edificações: medidas pela imagem de satélite retificada (≈), precisão ± 0,50 a 1,00 m.

Coordenadas dos vértices (UTM não aplicado): geográficas WGS-84, obtidas pelo ponto do Google Maps e pela imagem retificada.

Galpão principal: treliças metálicas a cada 5,00 m centro a centro (T1 a T9); lanternins, bloco alto e eólicos pela foto zenital do drone.

Sentidos de caimento indicados por setas - confirmar em campo antes de orçamento/projeto.

LEGENDA

- Cobertura da Moega 3 (medida em campo)
- Contorno de cobertura (imagem)
- Cumeeira
- Calha / água-furtada
- Sentido de caimento (a confirmar)
- Transportador / projeção

Unidades: metros (m) • Responsável técnico: _____

CLIENTE
TREVISAN - ARROZ

OBRA / LOCAL
COMPLEXO INDUSTRIAL - MOEGA 3

CONTEÚDO
DETALHES DE COBERTURA


SITUAÇÃO
LEVANTAMENTO PRELIMINAR - PARA CONFERÊNCIA

ESCALA
INDICADAS

DATA
25/09/2026


FOLHA
06/08

CORTES - PILARES, TRELIÇAS E LANTERNIM ELEVADO (NAVES 1, 2, 3 E BLOCO ALTO)

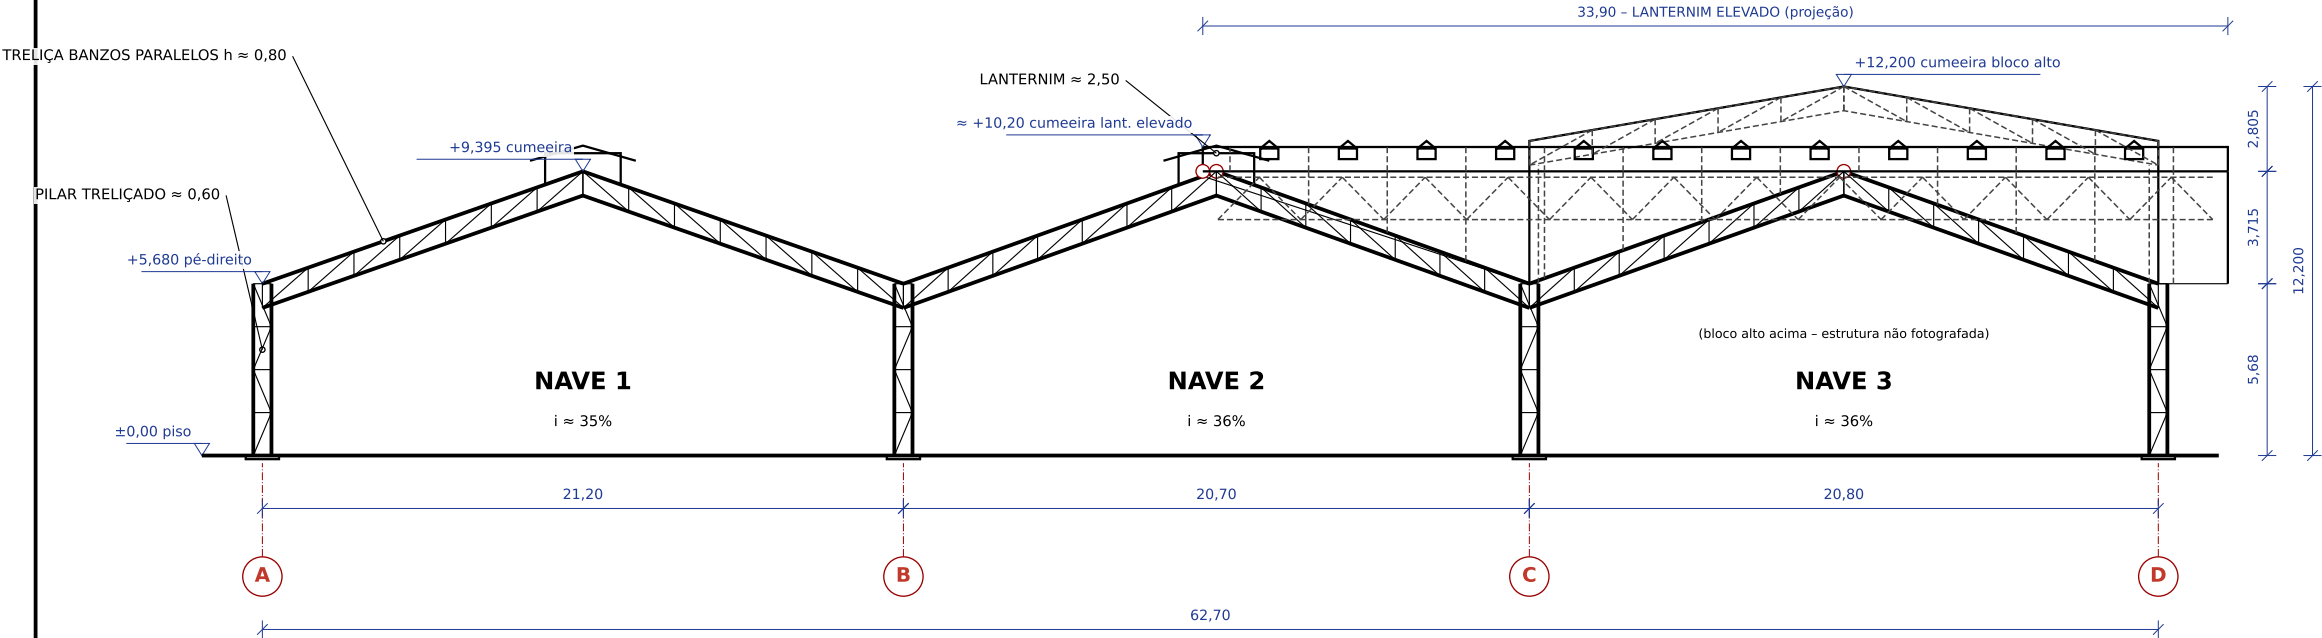


CORTE A-A - GALPÃO PRINCIPAL (transversal)

ESC. 1:250

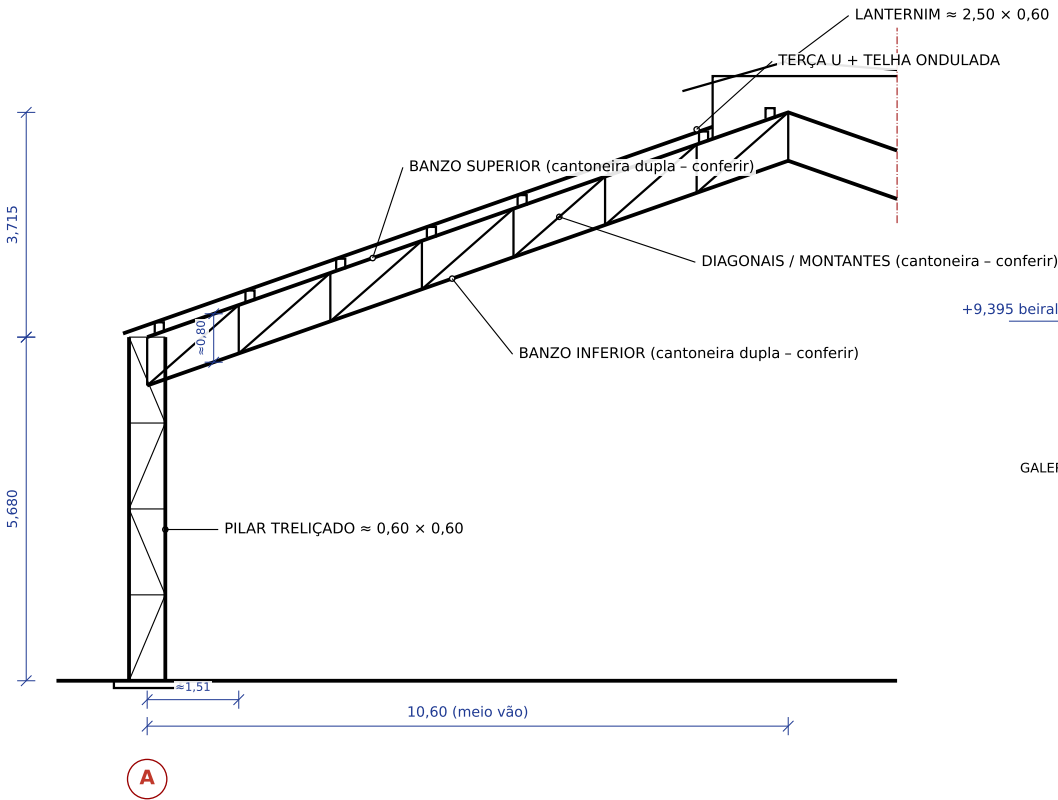


DETALHE 1 - TRELIÇA TÍPICA E LANTERNIM (Nave 1)

ESC. 1:125

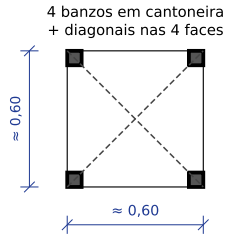

DET. 2 - PILAR

ESC. 1:33

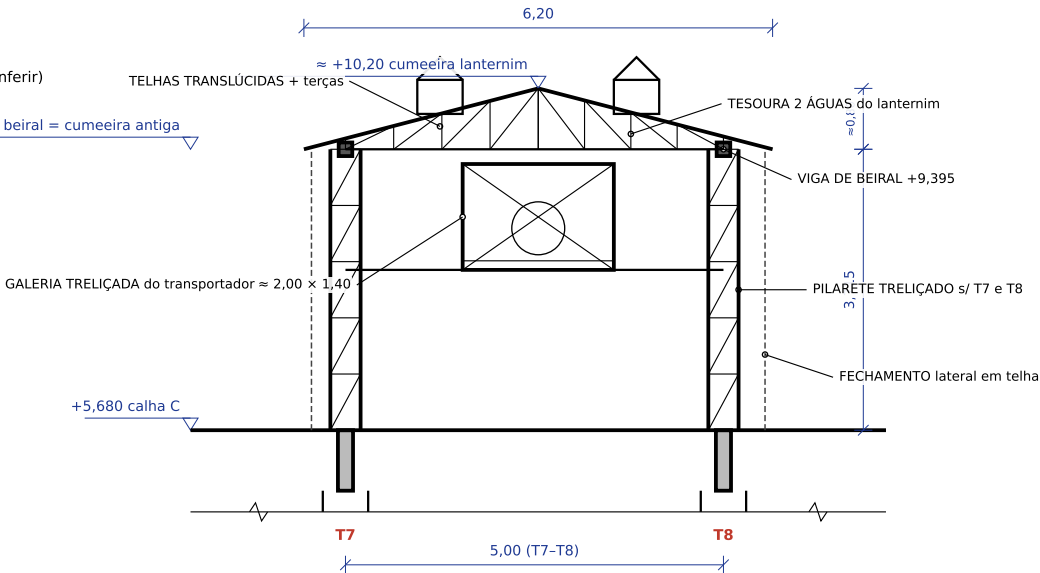

CORTE B-B - LANTERNIM ELEVADO (na calha C)

ESC. 1:100

NOTAS E PREMISSAS

Estrutura pelas fotos internas das Naves 1 a 3.
Alturas: rascunho de campo (IMG_4784):
pé-direito +5,680; cumeeira +9,395;
cumeeira do bloco alto +12,200.

Pilares metálicos TRELIÇADOS (4 banzos em cantoneira + diagonais), nas fachadas e nas linhas de calha entre naves (eixos A a D), um por treliça, a cada 5,00 c/c.

Treliças de cobertura de BANZOS PARALELOS inclinados (acompanham as águas), diagonais em N com montantes; apoio no topo dos pilares. Vigas treliçadas longitudinais no topo dos pilares; terças U sobre o banzo superior.

ESTIMADOS PELA FOTO (conferir em campo):
altura da treliça ≈ 0,80; pilar ≈ 0,60 x 0,60;
painéis ≈ 1,50; lanternim ≈ 2,50 x 0,60;
beiral do bloco alto ≈ +10,40; perfis.
Bloco alto: estrutura na folha 08.

LANTERNIM ELEVADO (33,90 x 6,20) c/ eólicos:
beirais exatamente na cumeeira do telhado antigo (+9,395 – pontos do drone), 2 águas no sentido norte-sul, cumeeira longitudinal ≈ +10,20.
Estruturado: pilaretes treliçados sobre T7 e T8 (nas calhas) e tesouras de 2 águas; fechamento lateral em telha; oitão leste até a Nave 3.
Internamente (fotos IMG_4734 a 4736): abriga a galeria treliçada galvanizada do transportador (≈ 2,00 x 1,40, piso em grade, ≈ +7,80 a +9,20) e tem faixas de telha translúcida – estimados.


LEGENDA

- Cobertura da Moega 3 (medida em campo)
- Contorno de cobertura (imagem)
- Cumeeira
- Calha / água-furtada
- Sentido de caimento (a confirmar)
- Transportador / projeção

Unidades: metros (m) • Responsável técnico: _____


CLIENTE TREVISAN - ARROZ		
OBRA / LOCAL COMPLEXO INDUSTRIAL - MOEGA 3		
CONTEÚDO ESTRUTURA METÁLICA - CORTE		
SITUAÇÃO LEVANTAMENTO PRELIMINAR - PARA CONFERÊNCIA		
ESCALA INDICADAS	DATA 25/09/2026	FOLHA 07/08

BLOCO ALTO (JUNTO À MOEGA) - ESTRUTURA METÁLICA

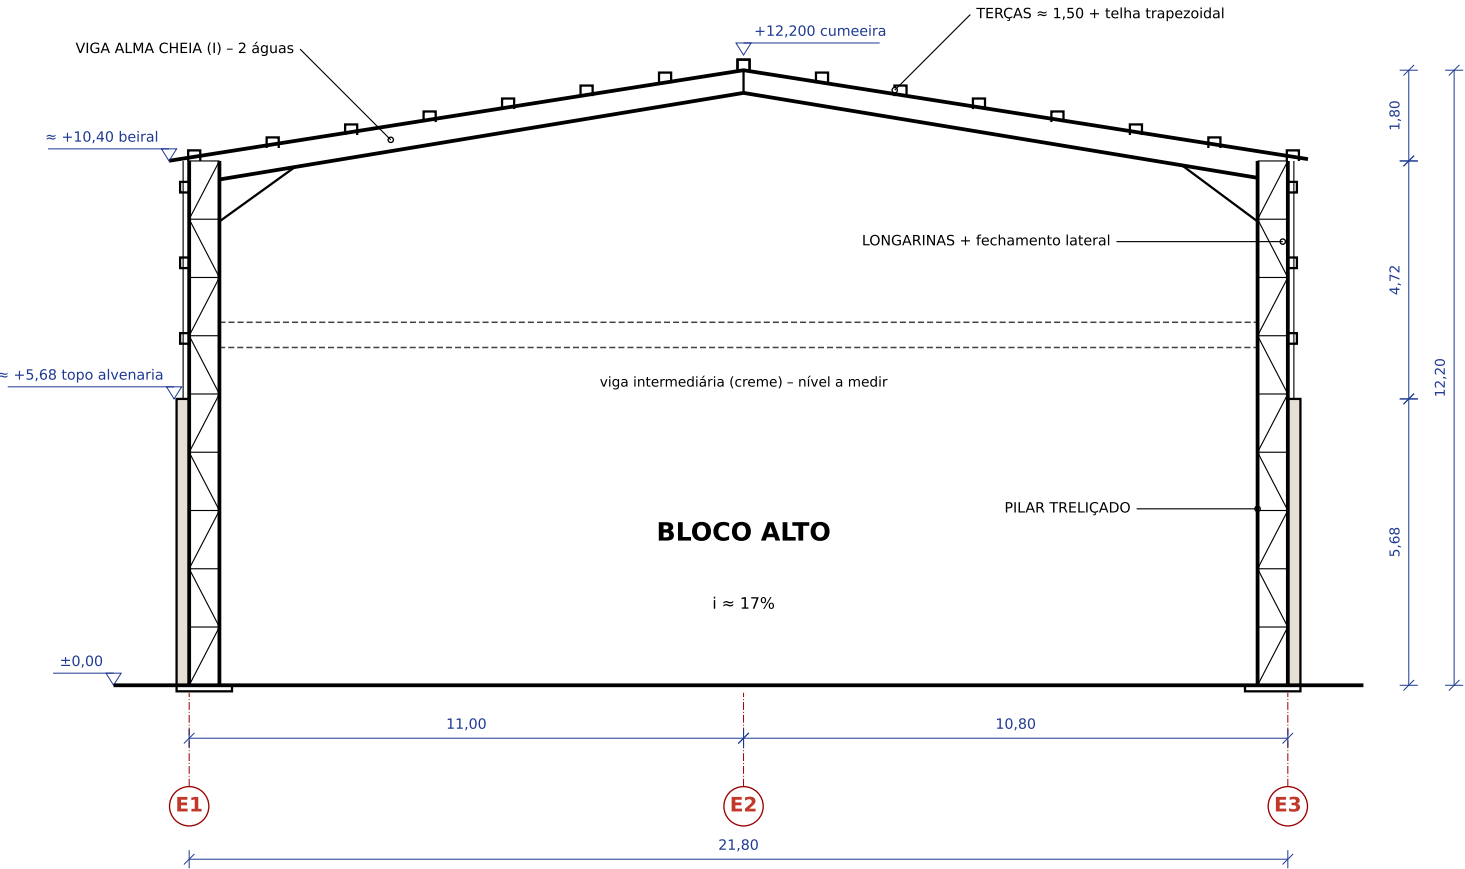

CORTE C-C - BLOCO ALTO (transversal)

ESC. 1:150

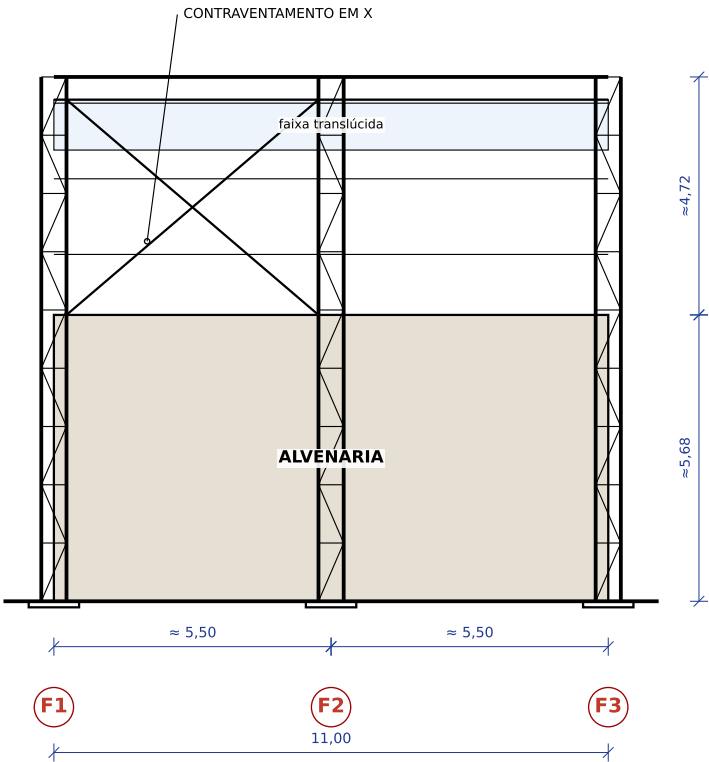

FACHADA LATERAL - 11,00

ESC. 1:150

NOTAS E PREMISSAS

BLOCO ALTO (≈ 21,80 × 11,00) ao lado da Moega 3, sobre a Nave 3 - fotos internas IMG_4723 a 4730.

Estrutura: pórticos metálicos com PILARES TRELIÇADOS (vermelhos) e VIGAS DE ALMA CHEIA (perfil I) em 2 águas; cumeeira no eixo central (x = 88,00) a +12,200 (rascunho de campo). Beiral ≈ +10,40 (proporção do rascunho).

Terças e longarinas metálicas (vermelhas) ≈ 1,50; fechamento em telha trapezoidal branca nas paredes e cobertura; faixa translúcida no alto das fachadas. Contraventamento em X nas paredes e barras na cobertura. Base em alvenaria até ≈ +5,68 (IMG_4730). Viga intermediária (creme) ≈ +7,20 (IMG_4728).

ESTIMADOS PELAS FOTOS - conferir em campo: beiral, nº de pórticos (≈ 5,50 c/c), perfis, espaçamento de terças/longarinas, níveis da viga intermediária e da alvenaria.

LEGENDA

- Cobertura da Moega 3 (medida em campo)
- Contorno de cobertura (imagem)
- Cumeeira
- Calha / água-furtada
- Sentido de caimento (a confirmar)
- Transportador / projeção

Unidades: metros (m) • Responsável técnico: _____

CLIENTE
TREVISAN - ARROZ

OBRA / LOCAL
COMPLEXO INDUSTRIAL - MOEGA 3

CONTEÚDO
BLOCO ALTO - ESTRUTURA

SITUAÇÃO
LEVANTAMENTO PRELIMINAR - PARA CONFERÊNCIA

ESCALA 1:150	DATA 25/09/2026	FOLHA 08/08
------------------------	---------------------------	-----------------------